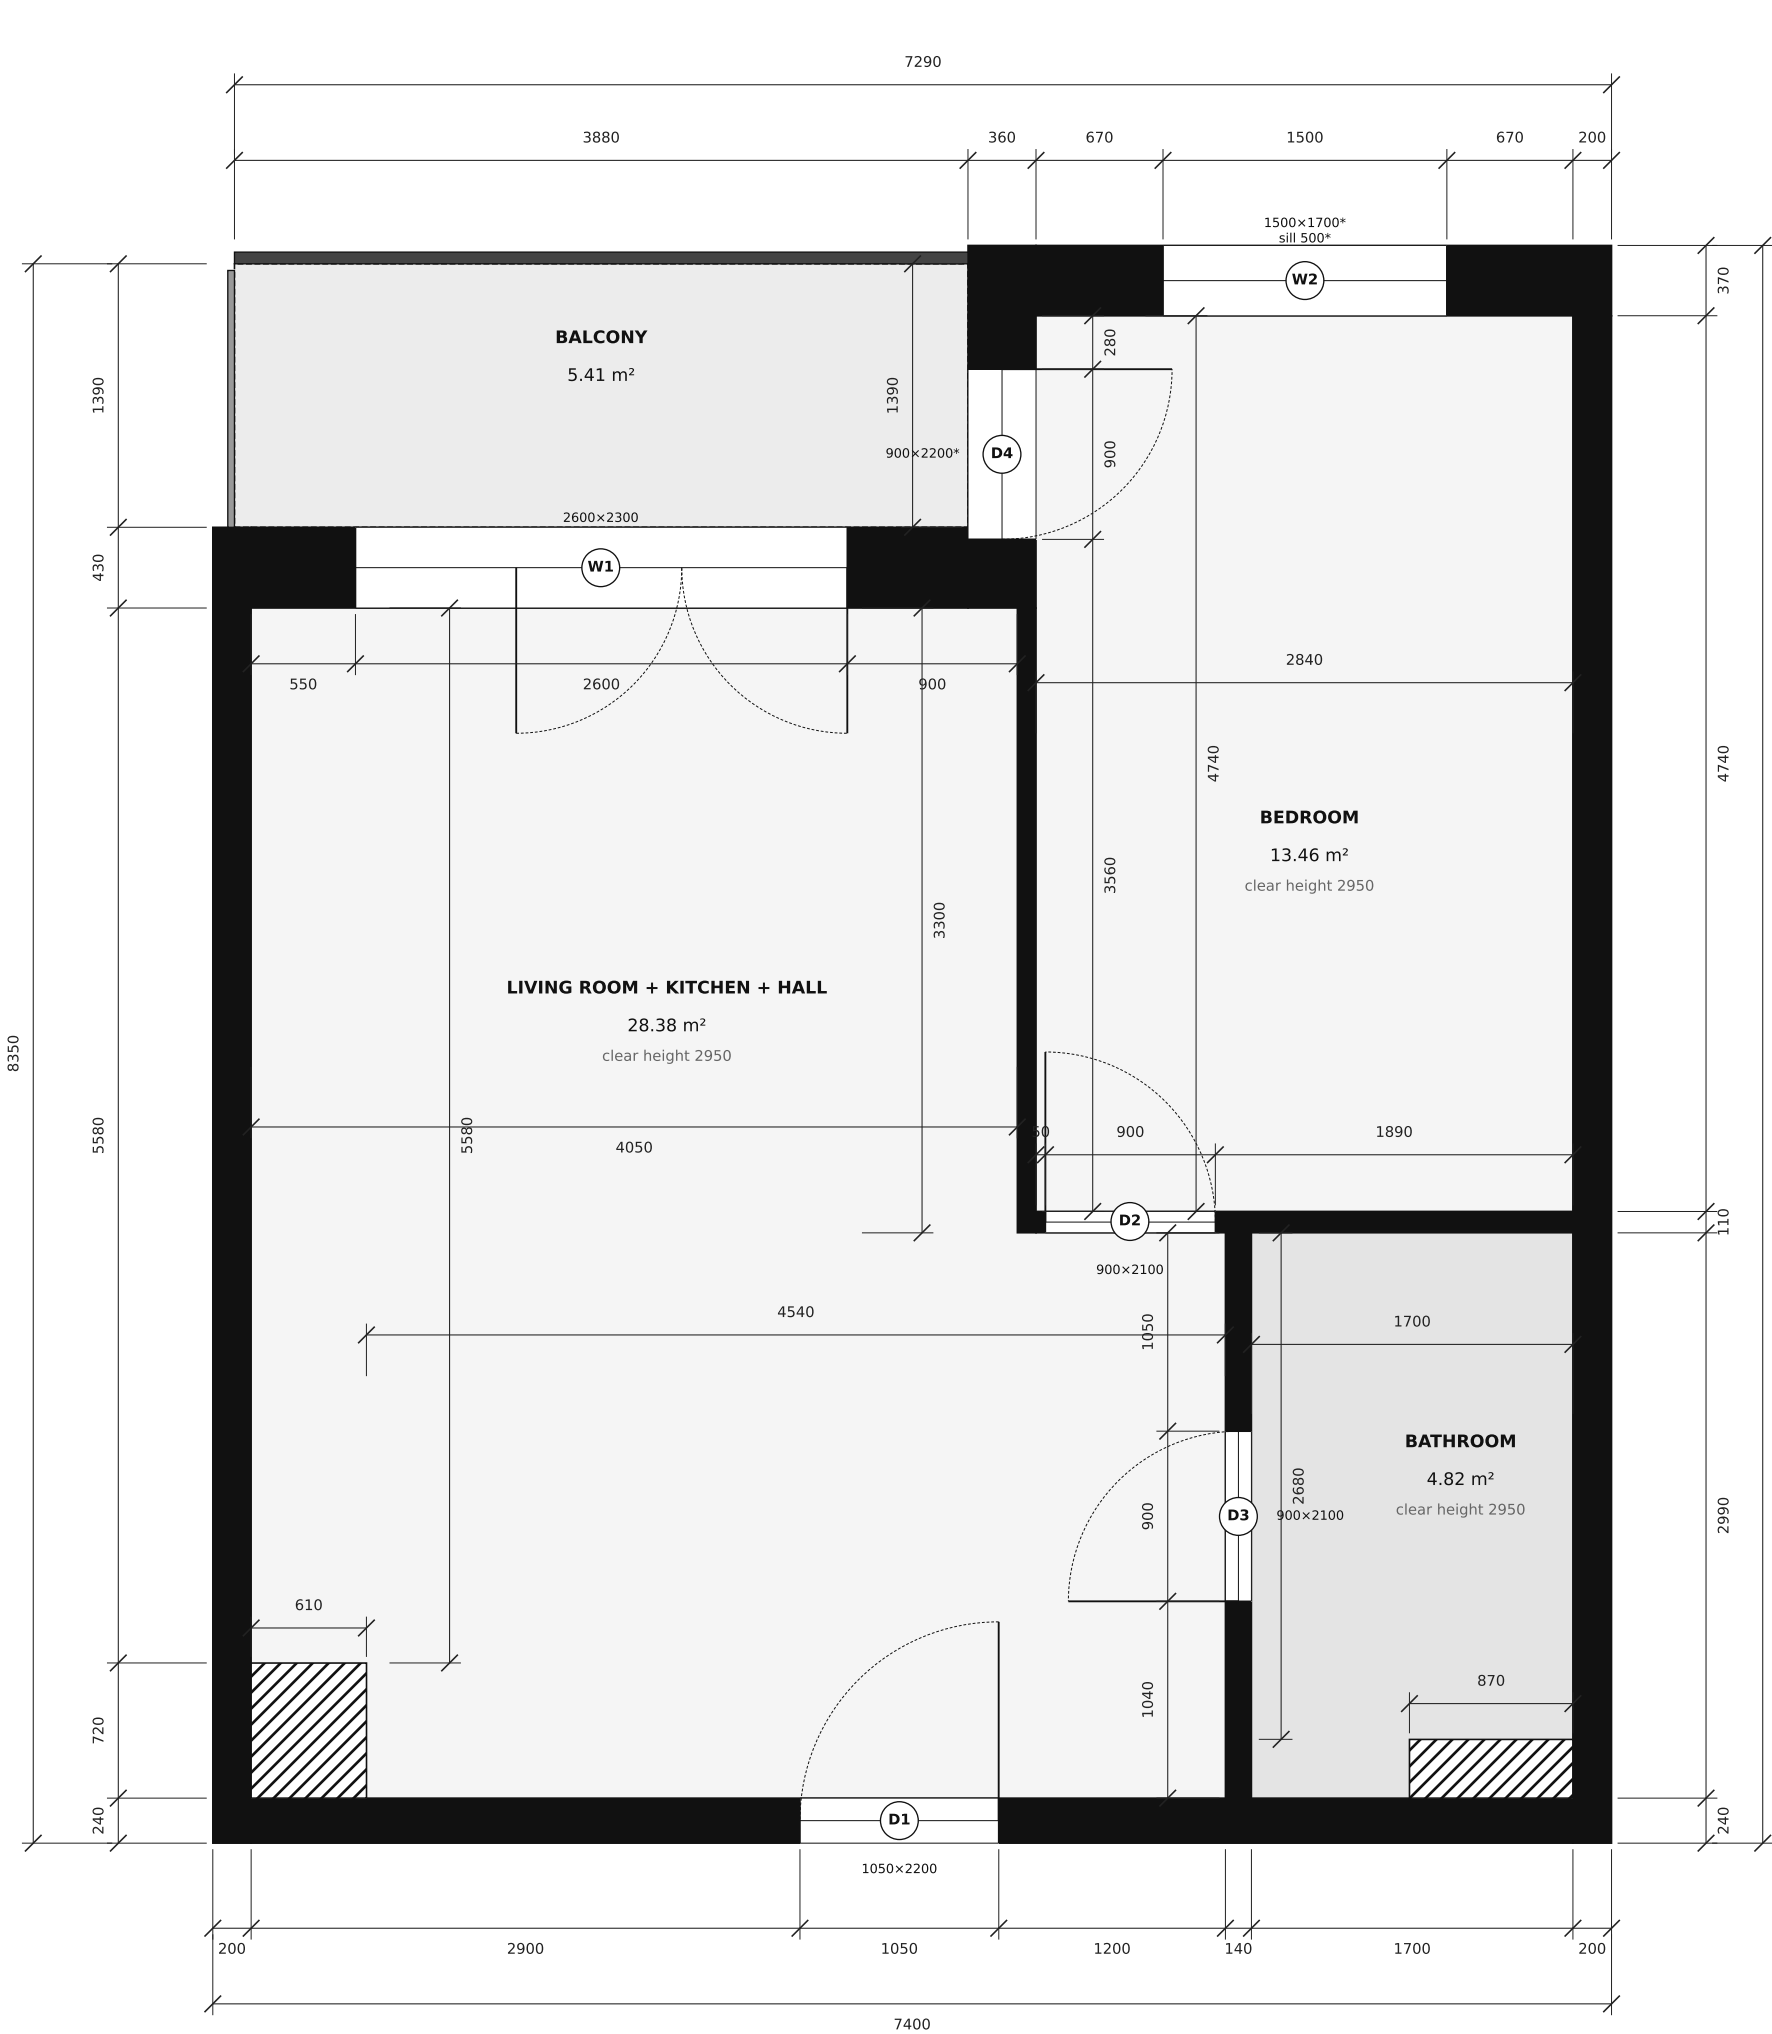


All dimensions in mm, rounded to 10. Measured from the plan's vectors, ±20 mm.
* = not printed on the plan, assumed (see the list below). Room dimensions are clear.

Openings					
Tag	Opening	Width	Height	Sill	Head
D1	entrance	1050	2200	0	2200
D2	bedroom door	900	2100	0	2100
D3	bathroom door	900	2100	0	2100
D4	bedroom balcony	900	2200*	0	2200*
W1	living balcony	2600	2300	0	2300
W2	bedroom window	1500	1700*	500*	2200*

Walls (shafts hatched)			
Wall	Type	Thickness	Length
W party west	party	200	6960
W ext living N	exterior	430	3790
W ext bedroom W	exterior	360	1920
W ext bedroom N	exterior	370	3050
W party east	party	200	8080
W corridor S	corridor	240	6990
P living bedroom	partition	100	3300
P bedroom S	partition	110	2840
P bath W	partition	140	2990
S kitchen shaft	shaft	610	710
S bath shaft	shaft	310	860

Rooms			
Room	Area m²	Clear height	Floor level
Living room + kitchen + hall	28.38	2950	finished floor ±0
Bedroom	13.46	2950	finished floor ±0
Bathroom	4.82	2950	finished floor ±0
Balcony	5.41	open	-50*
Total (rooms, not the usable area)	46.65		

- Assumed, to confirm**
- * window head: 2200 mm. Not on the plan; NEEDS CONFIRMATION.
 - * bedroom window sill: 500 mm. Plan says 'parapet obniżony' (lowered sill) with a low radiator; the height is not given. NEEDS CONFIRMATION.
 - * balcony floor offset: -50 mm. Balcony slab is usually a step below the interior floor; not on the plan.
 - * balcony railing: 1100 mm. Standard minimum railing height.
 - * floor above grade: 6800 mm. 2nd floor: ground floor raised ~0.3 m plus two storeys of ~3.25 m (2.95 m clear + slab). Not on the plan; only drives the view outside.

FLAT 19, BUILDING 18, WISZĄCE OGRODY




ul. Przytulna 1, Gdańsk · 2nd floor (II piętro)

TECHNICAL PLAN · DIMENSIONS

Source: developer's installation plan (DA-2a), 56.68 pt/m

Sheet 1/3

A3 · 1:40 · 2026-10-02

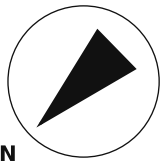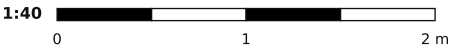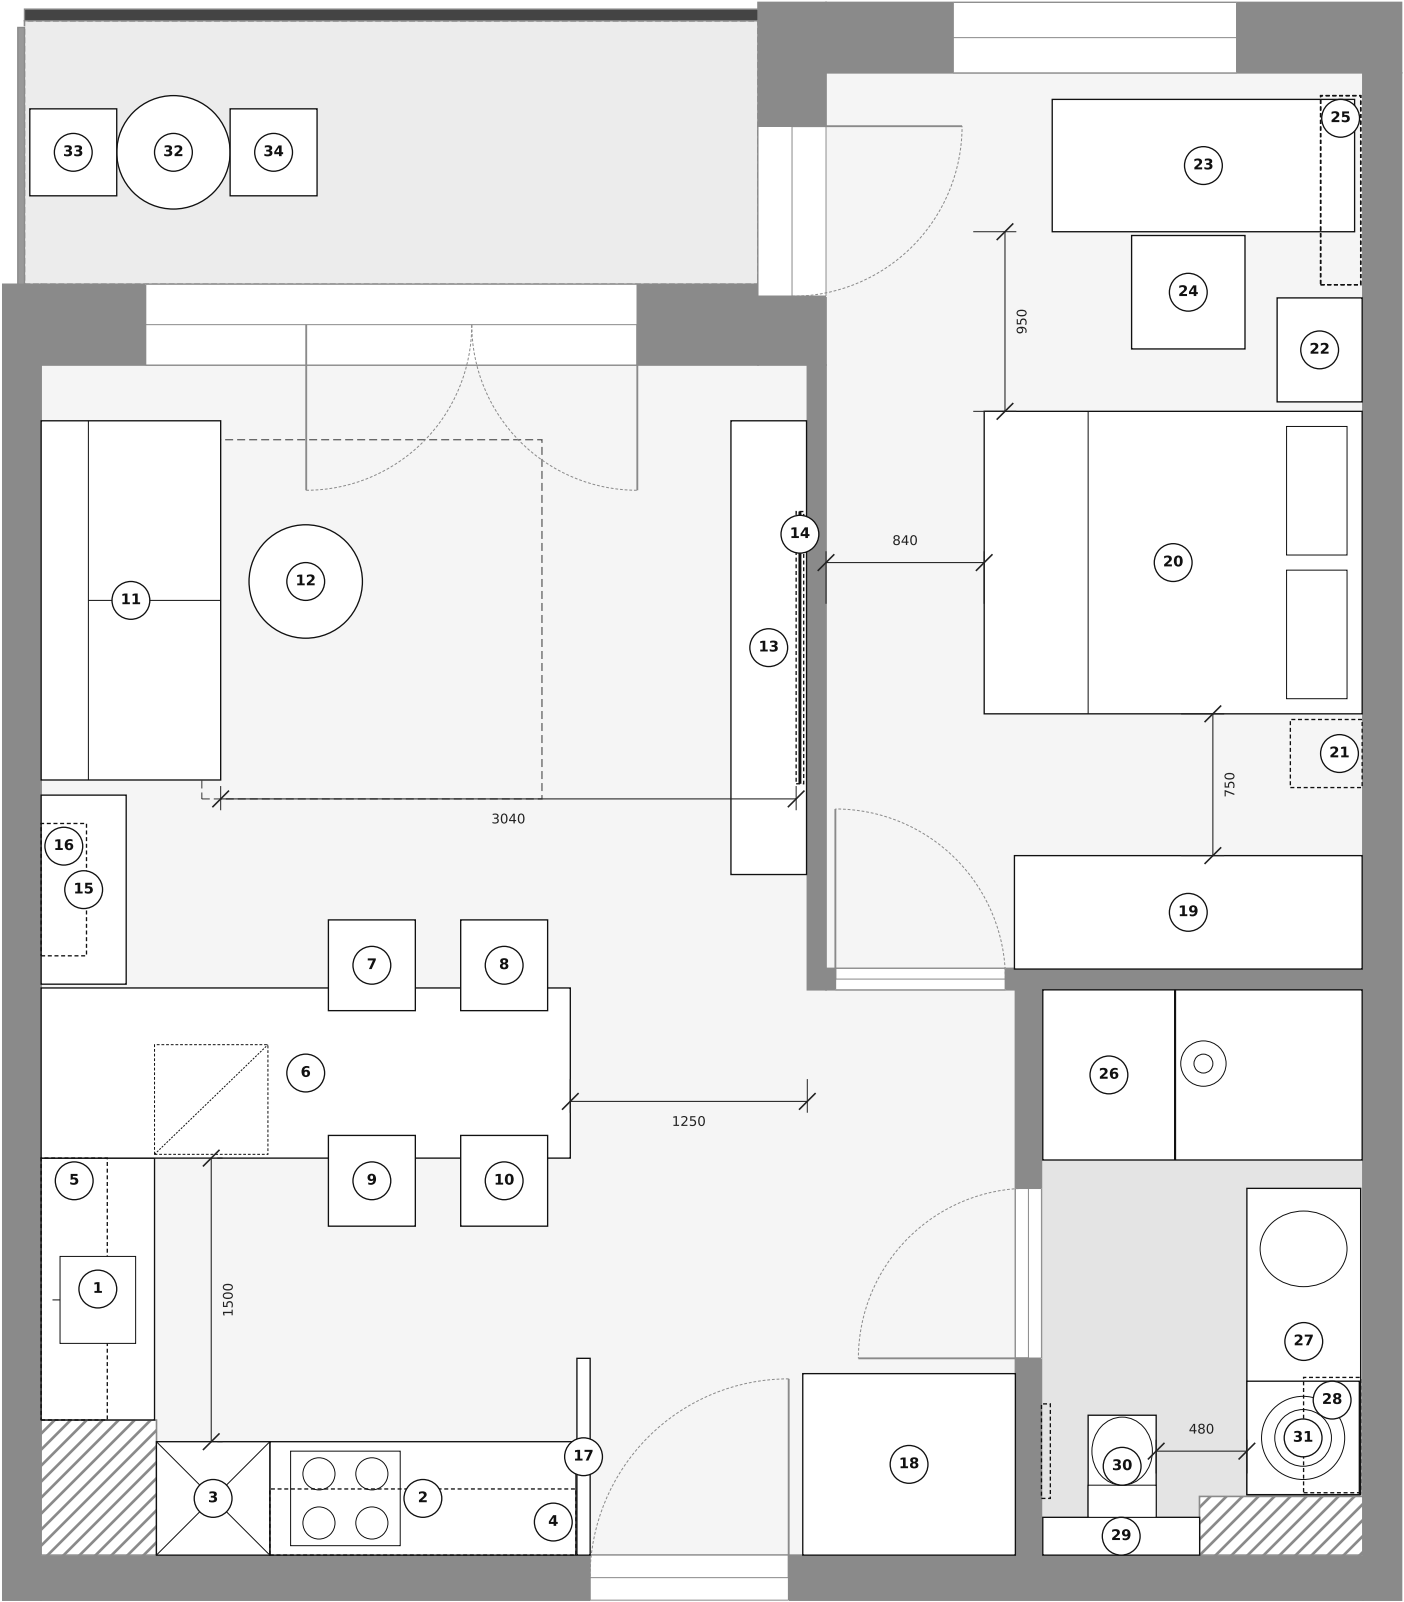

Sizes W × D × H in mm. X, Y = south-west corner of the footprint, from the inner SW corner of the living room.
Dashed outline = wall-mounted or hanging. Dashed grey = rug. Dimensions are clear distances between faces.

Furniture				
#	Item	W × D × H	X, Y	Bottom
1	Sink	600 × 1390 × 900	0, 720	0
2	Hob + oven	1620 × 600 × 900	1210, 0	0
3	Fridge	600 × 600 × 2850	610, 0	0
4	kitchen upper south	1620 × 350 × 1350	1210, 0	1500
5	kitchen upper west	350 × 1390 × 1350	0, 720	1500
6	Counter + table	2800 × 900 × 900	0, 2100	0
7	dining chair n1	460 × 480 × 800	1520, 2880	0
8	dining chair n2	460 × 480 × 800	2220, 2880	0
9	dining chair s1	460 × 480 × 800	1520, 1740	0
10	dining chair s2	460 × 480 × 800	2220, 1740	0
11	Sofa 190	950 × 1900 × 800	0, 4100	0
12	Round footrest	600 × 600 × 420	1100, 4850	0
13	Media wall	400 × 2400 × 2200	3650, 3600	0
14	tv	40 × 1440 × 830	4000, 4080	850
15	Sideboard	450 × 1000 × 800	0, 3020	0
16	sideboard shelf	240 × 700 × 30	0, 3170	1420
17	Oak slat screen	70 × 1040 × 2950	2840, 0	0
18	L wardrobe	1120 × 960 × 2850	4030, 0	0
19	Wardrobe (sliding)	1840 × 600 × 2850	5150, 3100	0
20	Bed 160x200	2000 × 1600 × 950	4990, 4450	0
21	bedside shelf s	380 × 360 × 50	6610, 4060	420
22	nightstand n	450 × 550 × 550	6540, 6100	0
23	Standing desk 160x70	1600 × 700 × 740	5350, 7000	0
24	desk chair	600 × 600 × 1200	5770, 6380	0
25a	bed shelf 1	210 × 1000 × 30	6770, 6720	1150
25b	bed shelf 2	210 × 1000 × 30	6770, 6720	1500
25c	bed shelf 3	210 × 1000 × 30	6770, 6720	1850
26	Rain shower 170x90	1690 × 900 × 2650	5300, 2090	0
27	Basin	600 × 1620 × 900	6380, 320	0
28	bath cabinet	300 × 610 × 700	6680, 330	1450
29	wc frame boxing	830 × 200 × 1200	5300, 0	0
30	WC	360 × 540 × 420	5540, 200	0
31	Washer	590 × 600 × 850	6380, 320	0
32	Bistro	600 × 600 × 720	400, 7120	0
33	balcony chair w	460 × 460 × 860	-60, 7190	0
34	balcony chair e	460 × 460 × 860	1000, 7190	0

FLAT 19, BUILDING 18, WISZĄCE OGRODY




ul. Przytulna 1, Gdańsk · 2nd floor (II piętro)

FIT-OUT PLAN · FURNITURE AND CLEARANCES

Source: developer's installation plan (DA-2a), 56.68 pt/m

Sheet 2/3

A3 · 1:40 · 2026-10-02

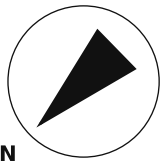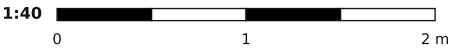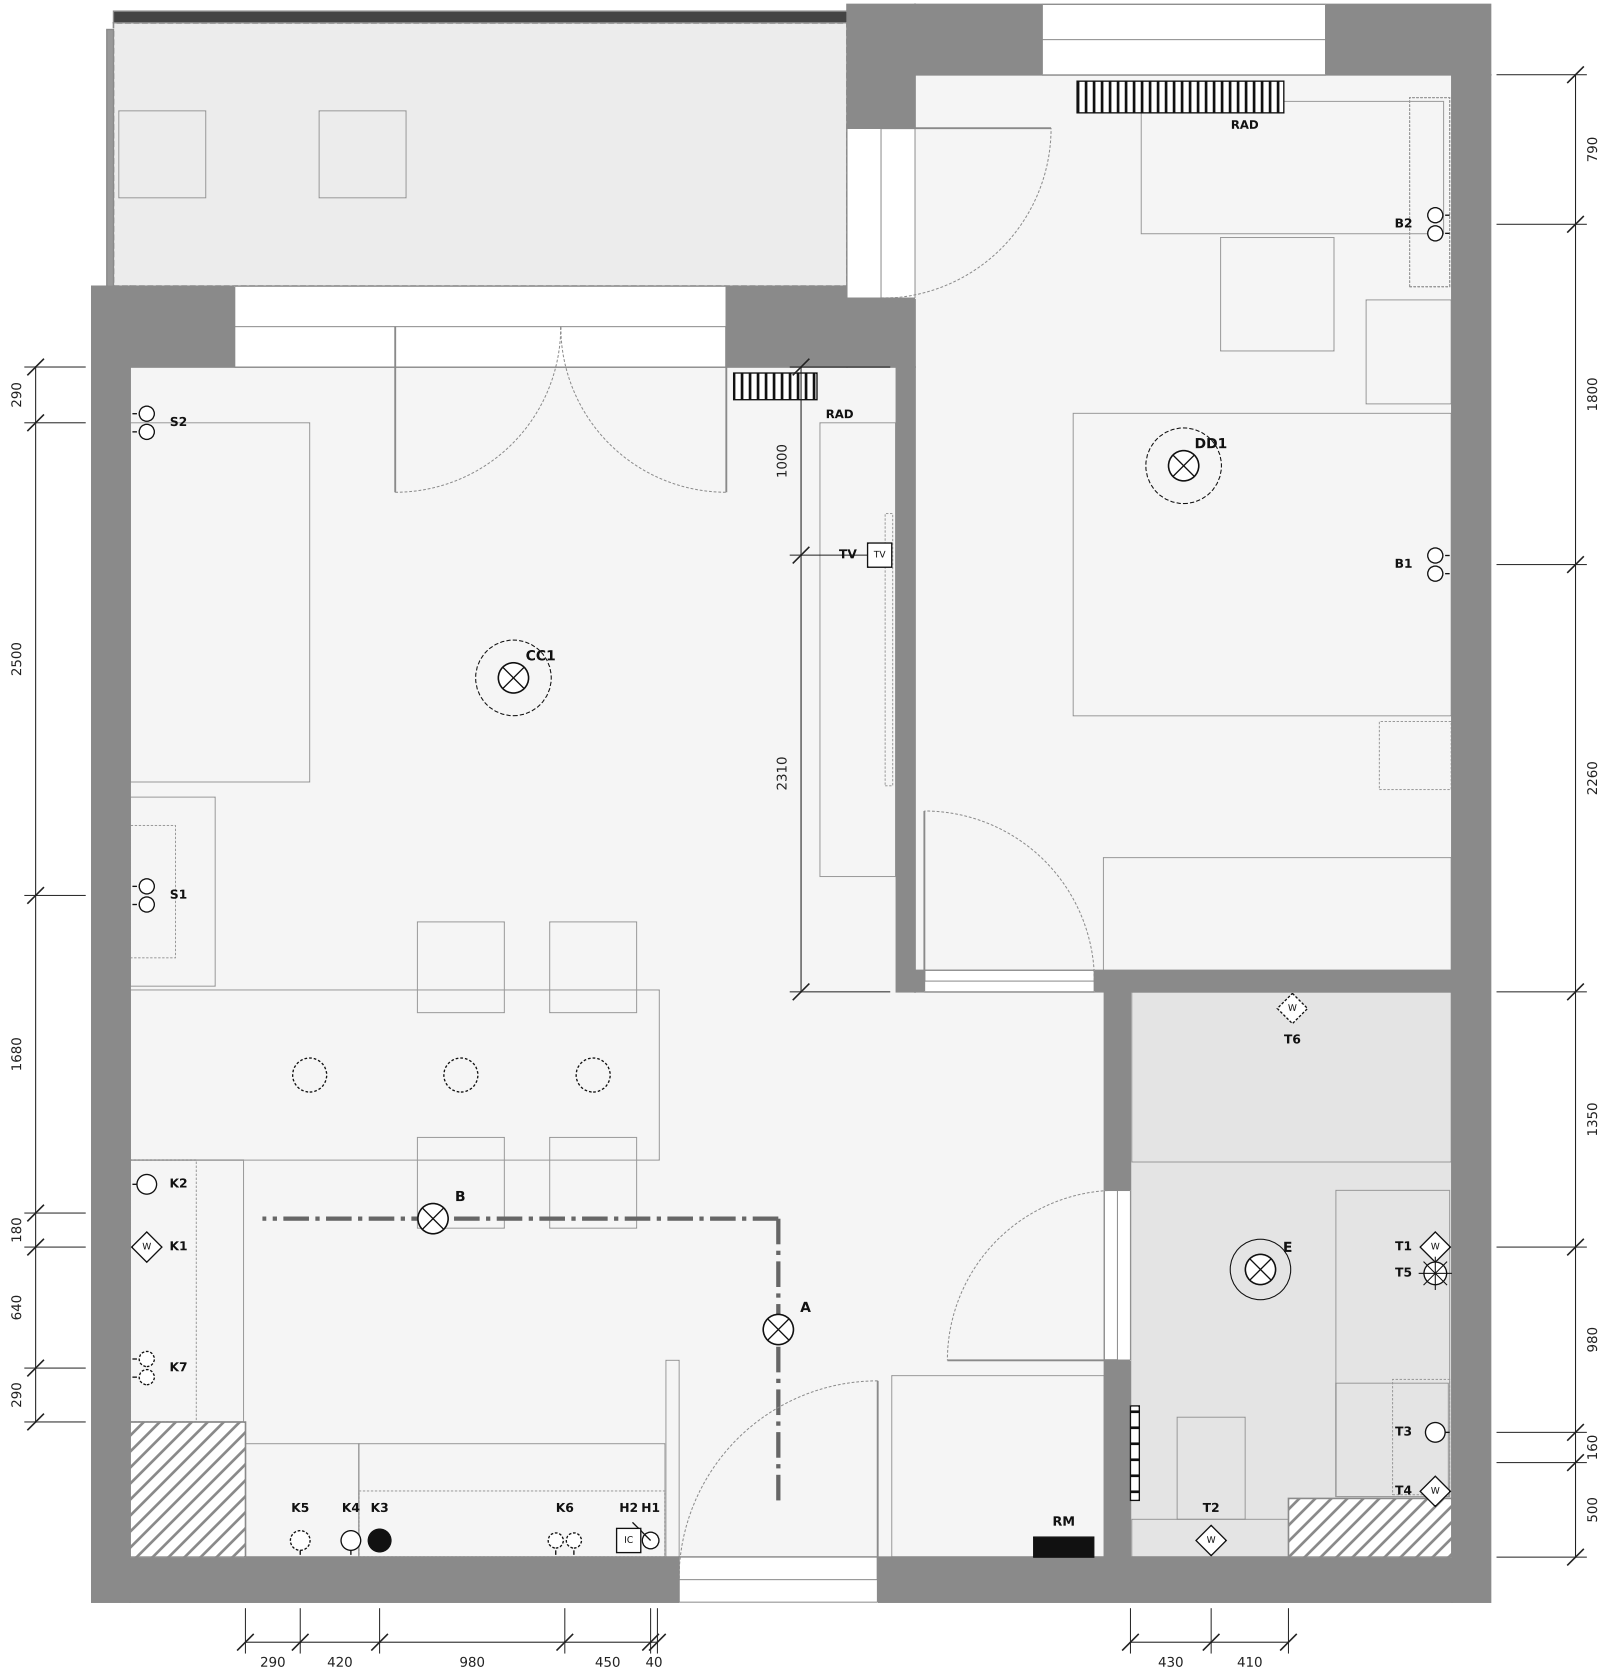

X, Y from the inner SW corner of the living room, in mm. h = height above the finished floor.
* = height not printed on the plan, set by convention. PROPOSED = not on the developer's plan, to confirm.

Points					
ID	Point	Room	X, Y	h	Source
S1	Double socket 230 V	living	0, 3500	300*	plan
S2	Double socket 230 V	living	0, 6000	300*	plan
TV	TV / SAT / data + socket	living	4050, 5300	500*	plan
K1	Water supply and drain	kitchen	0, 1640	500*	plan
K2	Socket 230 V	kitchen	0, 1820	300*	plan
K3	Socket 400 V	kitchen	1320, 0	300*	plan
K4	Socket 230 V	kitchen	1320, 0	2000	plan
K5	Socket 230 V	kitchen	900, 0	300*	PROPOSED
K6	Double socket 230 V	kitchen	2300, 0	1100*	PROPOSED
K7	Double socket 230 V	kitchen	0, 1000	1100*	PROPOSED
H1	Light switches A, B	hall	2750, 0	1100	plan
H2	Intercom	hall	2790, 0	1600	plan
B1	Double socket 230 V	bedroom	6990, 5250	300*	plan
B2	Double socket 230 V	bedroom	6990, 7050	300*	plan
T1	Water supply and drain	bathroom	6990, 1640	500*	plan
T2	Water supply and drain	bathroom	5720, 0	200*	plan
T3	Socket 230 V	bathroom	6990, 660	700	plan
T4	Water supply and drain	bathroom	6990, 500	700	plan
T5	Wall light outlet	bathroom	6990, 1650	2300	plan
T6	Water supply and drain	bathroom	6150, 2990	1100*	PROPOSED
A	Ceiling light outlet	hall	3430, 1200	2950	plan
B	Ceiling light outlet	kitchen	1600, 1790	2950	plan
CC1	Ceiling light outlet	living room	2030, 4650	2950	plan
DD1	Ceiling light outlet	bedroom	5570, 5770	2950	plan
E	Ceiling light outlet	bathroom	5980, 1520	2950	plan

Notes

TV: TV / SAT / internet with a double socket, on the media wall

K5: Fridge, in the tall unit

K6: Worktop, splashback

K7: Worktop, west run

H1: Light switches A and B, h 1.10 m, 15 cm from the entrance opening. Conflict with the kitchen run: move onto the slat screen post (see docs/flat.md)

T6: Shower mixer; the rain head is at X 6.15, Y 2.60, h 2.20. The plan draws a bathtub, not a shower

Dining pendants (dashed circles) are not on an outlet: they need a cable from outlet B. LED profile runs A, then B.

Kitchen shaft: sewer stack, ventilation and the hood duct. Bath shaft: behind the washing machine and basin.

Radiators (hatched) are fixed by the developer. Only the points on the plan are measured; other switches are not on it.

Key

socket 230 V

double socket

socket 400 V

TV / SAT / data

dashed = proposed (not on the plan)

light switch

intercom

water + drain

wall light

FLAT 19, BUILDING 18, WISZĄCE OGRODY

ul. Przytulna 1, Gdańsk · 2nd floor (II piętro)

SERVICES · SOCKETS, SWITCHES, WATER, LIGHTS

Source: developer's installation plan (DA-2a), 56.68 pt/m

Sheet 3/3

A3 · 1:40 · 2026-10-02