


ILOŚĆ POMIESZCZEŃ WPISANYCH DO KSIĘGI WIECZYSTEJ I DO AKTU NOTARIALNEGO PRZENOSZĄCEGO WŁASNOŚĆ LOKALU BĘDZIE POKRYWAŁA SIĘ Z BIEŻĄCĄ KARTĄ INSTALACYJNĄ MIESZKANIA (z naniesionymi zmianami w układzie ścianek działowych)

- ELEMENTY WYPOSAŻENIA NIEPODLEGAJĄCE ZMIANOM ARANŻACYJNYM:
- grzejniki - płytowe stalowe, grzejnik rurkowy w pomieszczeniu łazienki - kolor biały
  - parapety - konglomerat kamienny
  - stolarka okienna - PCV
  - wylewki betonowe - pod panele, płytki, wykładzinę

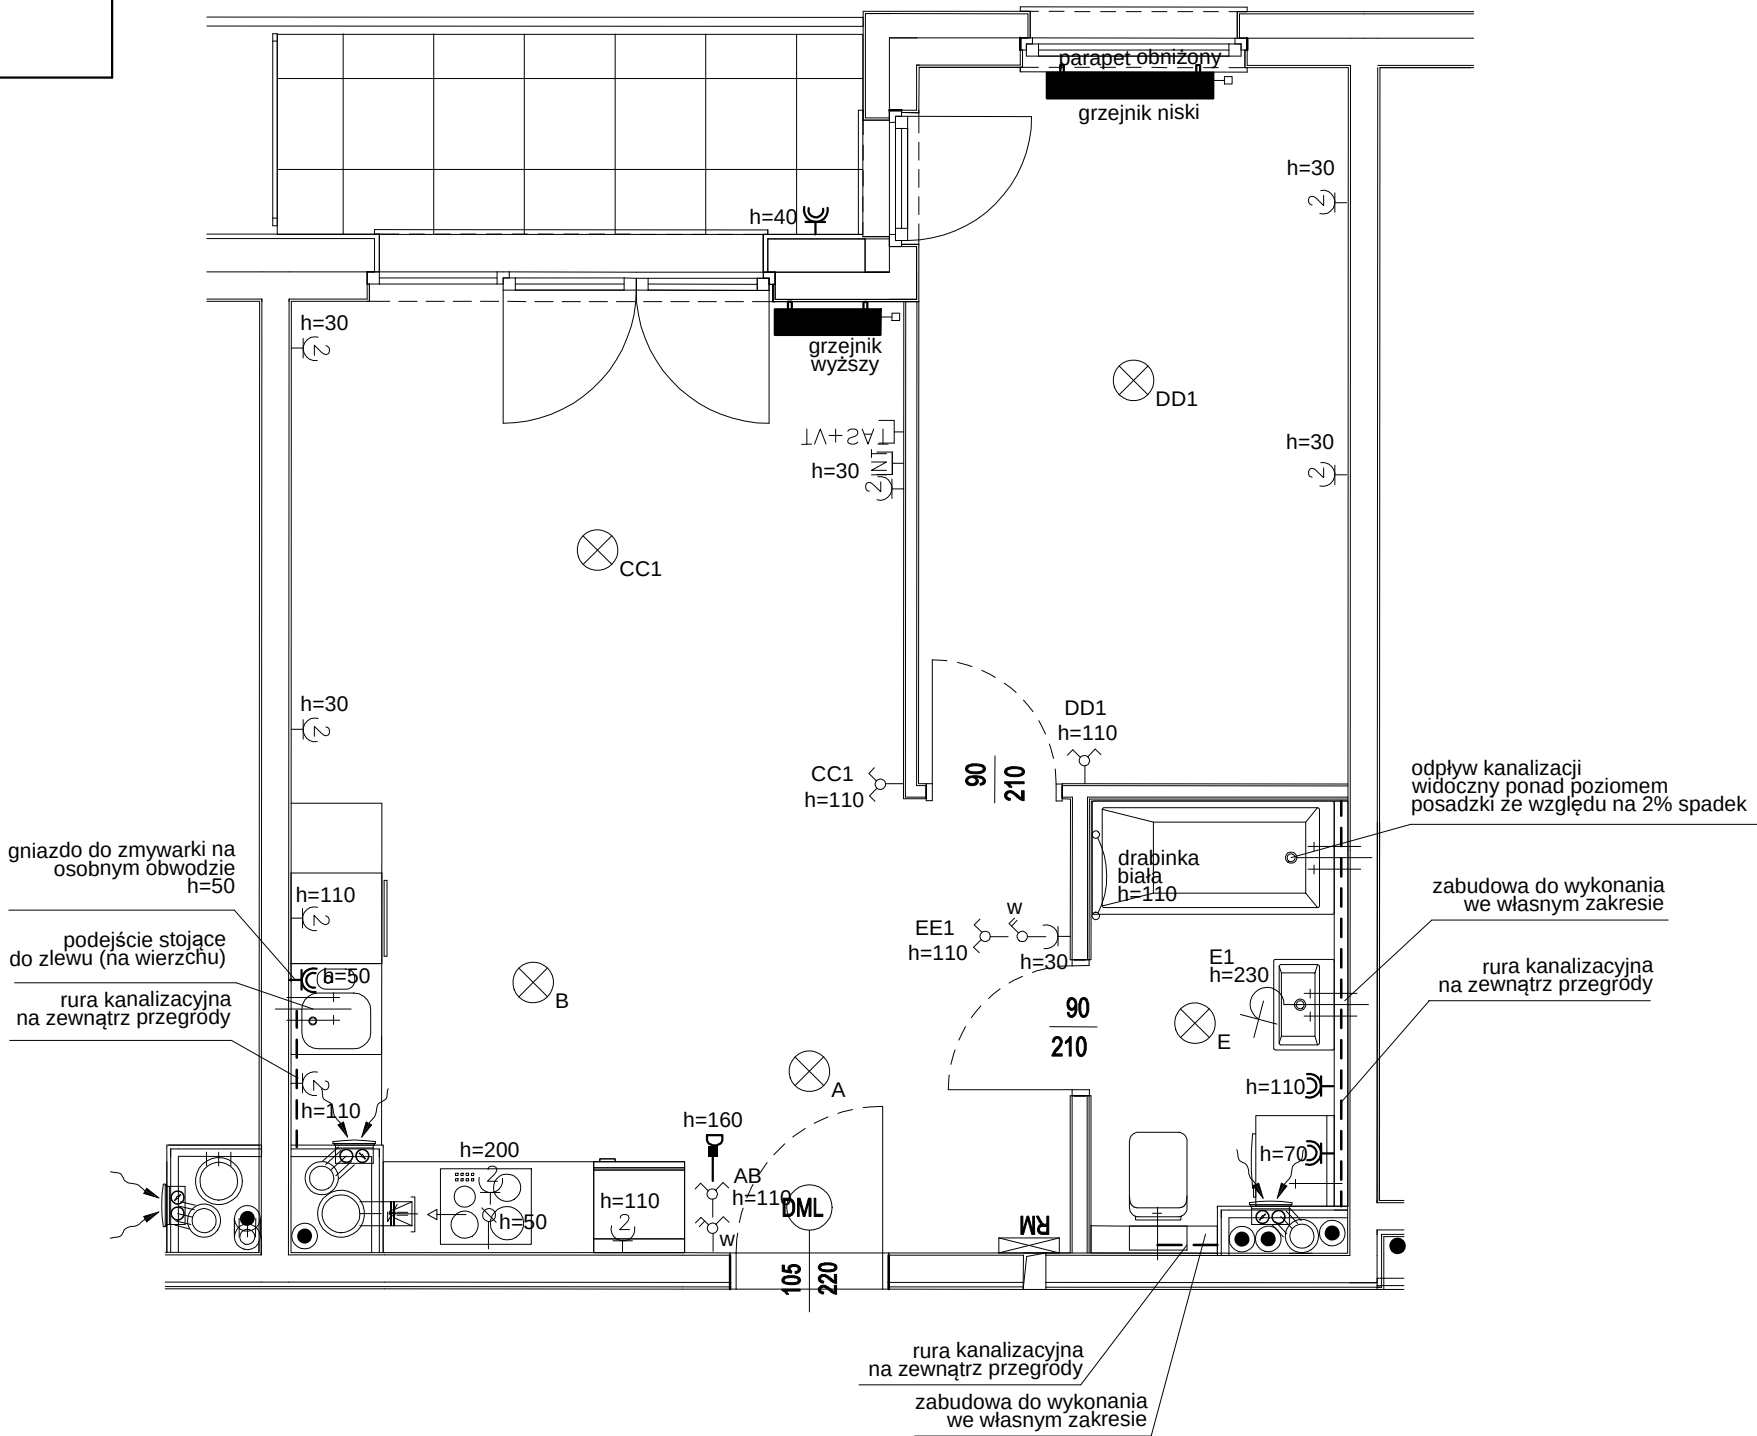

- UWAGI :
- ŁĄCZNIKI ŚWIATŁA h=110cm
  - GNIAZDA ZASILAJĄCE W POKOJACH h=30cm LUB ZGODNIE Z OPISEM
  - ŁĄCZNIKI ŚWIATŁA - OŚ 15cm OD KRAWĘDZI ŚCIANY LUB OTWORU DRZWIOWEGO
  - W PRZYPADKU ELEMENTÓW ELEKTRYCZNYCH ZLOKALIZOWANYCH PIONOWO NAJNIŻEJ W RAMCE UMIESZCZAMY ELEMENT NARYSOWANY NAJBLIŻEJ ŚCIANY (NA RZUCIE)
  - ŚCIANKI DZIAŁOWE - GIPSOWO-KARTONOWE
  - OTWORY DRZWIOWE O WYMIARACH 90x210

- ŁAZIENKA:
- wc wiszące - podejście na wierzchu, zabudowa do wykonania we własnym zakresie
  - umywalka - podejście stojące na wierzchu
  - wanna - podejście ściennie
  - pralka - podejście wodne na wierzchu

LEGENDA:

INSTALACJA ELEKTRYCZNA :

Gniazdo wtyczkowe

Gniazdo wtyczkowe o IP X4

Wypust 400V (SIŁA)

Gniazdo telewizyjne RTV

Domofon ze słuchawką

Gniazdo Internet

Skrzynka bezpiecznikowa i teletechniczna

Łącznik pojedynczy

Łącznik podwójny

Łącznik krzyżowy

Wypust sufitowy

Wypust ścienny

INSTALACJA HYDRAULICZNA / C.O. :

grzejnik (nie w skali)


podejście podwójne

podejście pojedyncze

podejście z.w. na taras / ogródek


Załącznik DA-2a

Deweloper nie udostępnia planów z wymiarami. Wymiary do odczytu wyłącznie ze skali.

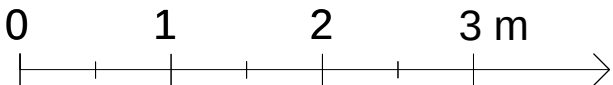

Deweloper zastrzega sobie prawo do zmian w projekcie. Zmian lokalizacji wyjść instalacji elektrycznych, wod-kan, c.o. ze względu na umiejscowienie i charakter elementów konstrukcyjnych, wymiary mogą ulec zmianie w trakcie budowy.

SZACHT INSTALACYJNY - OZNACZENIA:

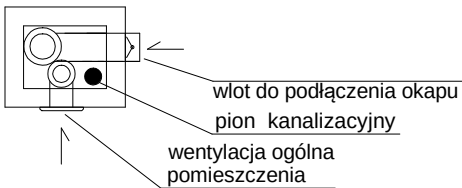

## KARTA INSTALACYJNA

WISZĄCE OGRODY  
Gdańsk  
ul. Przytulna 1

| budynek | mieszkanie | piętro |
|---------|------------|--------|
| 18      | 19         | 2      |

Opracowanie: A. Płóciennik